



Турківська районна рада

РАЙОННИЙ АРХІТЕКТОР

Будівельний паспорт на забудову земельної ділянки виділеної індивідуальному забудовнику

ЯВОРСЬКОМУ АМТРУ ОСИПОВИЧУ

(прізвище, ім'я та по батькові)

в місті
(селі)

ЯВОРА

по вул.

буд. № _____ Турківського району

ЗМІСТ

1. Ухвала міської, селищної, сільської Ради.
2. Проект забудови земельної ділянки.
3. Схема розміщення земельної ділянки в системі забудови.
4. Схема виносу в натуру меж земельної ділянки і розбивки вісей будівель.
5. Проект житлового будинку.
6. Пояснювальна записка до проекту забудови земельної ділянки.
7. Акт виносу в натуру меж земельної ділянки і розбивки вісей будівель.
8. Обов'язки індивідуального забудовника.
9. Дозвіл інспектора ДАБК на право закладки фундаментів під індивідуальне будівництво.
10. Акт прийняття фундаментів.
11. Акт прийняття в експлуатацію індивідуального будівництва.

ПРИМІТКА: Документи зазначені в пунктах 9-11 видаються після отримання Державного акту на право власника землею.

ЯВІРСЬКА СІЛЬСЬКА РАДА

4 – сесія

5 – скликання

РІШЕННЯ № 99

Від 16 січня 2007 року.

Про надання дозволу на будівництво житлового будинку на власній присадибній ділянці жителю м. Борислав Яворському Дмитру Осиповичу

Розглянувши заяву гр. Яворського Д.О., та керуючись статтями 121,123 Земельного Кодексу України про надання дозволу на будівництво житлового будинку на власній присадибній ділянці в с. Явора на урочищі "Варуш" та погодження проекту детального планування території (кварталу) розробленим Турківським районним ЗКБ сесія Явірської сільської ради

ВИРІШИЛА:

1. Надати дозвіл гр. Яворському Д.О. жителю м. Борислава, на будівництво житлового будинку на власній присадибній ділянці згідно схеми кварталу в с. Явора на урочищі "Варуш"
2. Гр. Яворському Д.О. приступити до будівництва житлового будинку після погодження в органах архітектури проекту на будівництво.
3. Землевпоряднику при Явірській сільській раді внести зміни в земельно-облікові документи.
4. Завершений будівництвом індивідуальний будинок здати в експлуатацію.

Сільський голова:




С.ІГНАЦЕВИЧ

земельної ділянки №

Масштаб 1:500

• Масштаб 1:500

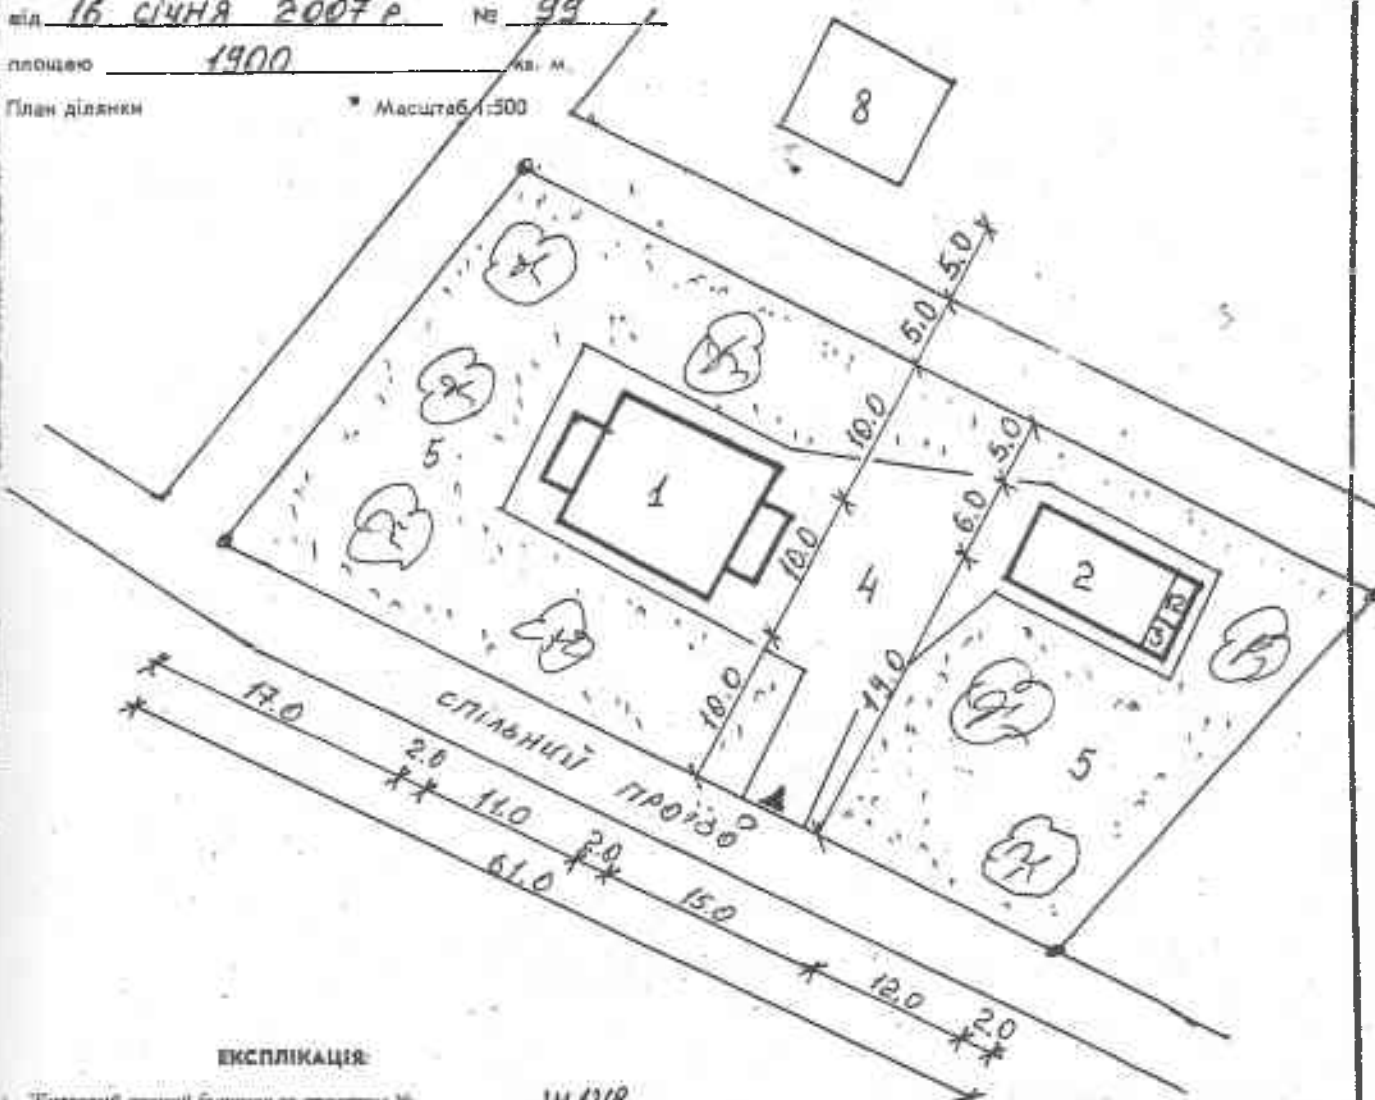

ЕКСПЛІКАЦІЯ

1. Житловий двоповерховий будинок за проектом №
2. Господарська будівля за проектом №
3. Убиральня
4. Подвір'я
5. Город-Сад
6. Кітник
7. Будівлі, які підлягають знесенню
8. Сусідні будівлі
9. Проректовані будівлі
10. Лох
11. Літня кухня
12. Витонена загірібна жид
13. Гараж
14. Веранда

141218

140113

ПРОЕКТНО-ВИРОБНИЧИЙ
АРХІТЕКТУРНО-ПЛАНУВАЛЬНИЙ ВІДДІЛ

Зав. відділом	ІВНИЦЬКА	Масштаб
Виконав	Р. ЛОФІГІ	Дата
Перевірено	ІВНИЦЬКА	Реєстр №


ПОГОДЖЕНО:

ЗАСТУПНИК ГОЛОВНОГО АРХІТЕКТОРА
Львівської області
О.В.Матвій

ПРОЕКТ
ОДНОКВАРТИРНОГО
ОДНОПОВЕРХОВОГО
ЧОТИРИКІМНАТНОГО
ЖИТЛОВОГО
БУДИНКУ
З МАНСАРДОЮ

КОШТОРИСНА ВАРТІСТЬ _____ 9 тис. 800 крб
ЖИТЛОВА ПЛОЩА _____ 598 м²
КОРИСНА ПЛОЩА _____ 935 м²
ДОДАТКОВА ПЛОЩА _____ 335 м²
ПЛОЩА ЗАБУДОВИ _____ 1090 м²
БУДІВЕЛЬНИЙ ОБ'ЄМ _____ 465,6 м³


УПРАВЛІННЯ В СПРАВАХ БУДІВНИЦТВА І АРХІТЕК- ТУРИ ЛЬВІВСЬКОГО ОБЛАВІКОНКОМУ	ОБ-М-4/79	
ТЕХНІЧНИЙ ВІДДІЛ	ФАСАДИ, ПЛАНИ ПОВЕРХІВ	
СЕКТОР ВІДВОДІВ ЗЕМЕЛЬНИХ ДІЛЯНОК		
НАЧАЛЬНИК ВІДДІЛУ		ГЛОШНИК З.П. 1970
НАЧАЛЬНИК СЕКТОРУ		ЛИТВИН В.В.
АВТОР ПРОЕКТУ		ЛИТВИН В.В.
		1979
ПЕРЕВІРИВ		МЕТЕРА В.А.

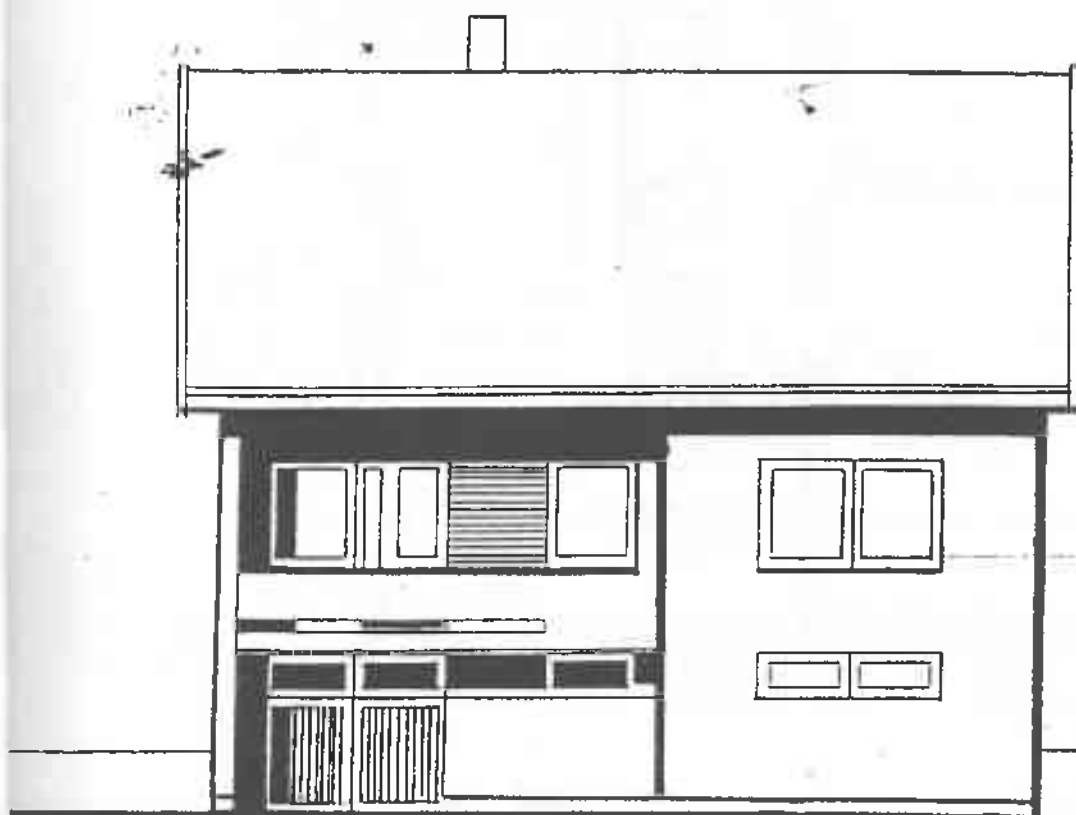


ПЛАН ЦОКОЛЬНОГО ПОВЕРХУ -2.40


ОБ.М.4/79

ПІВНІЧ

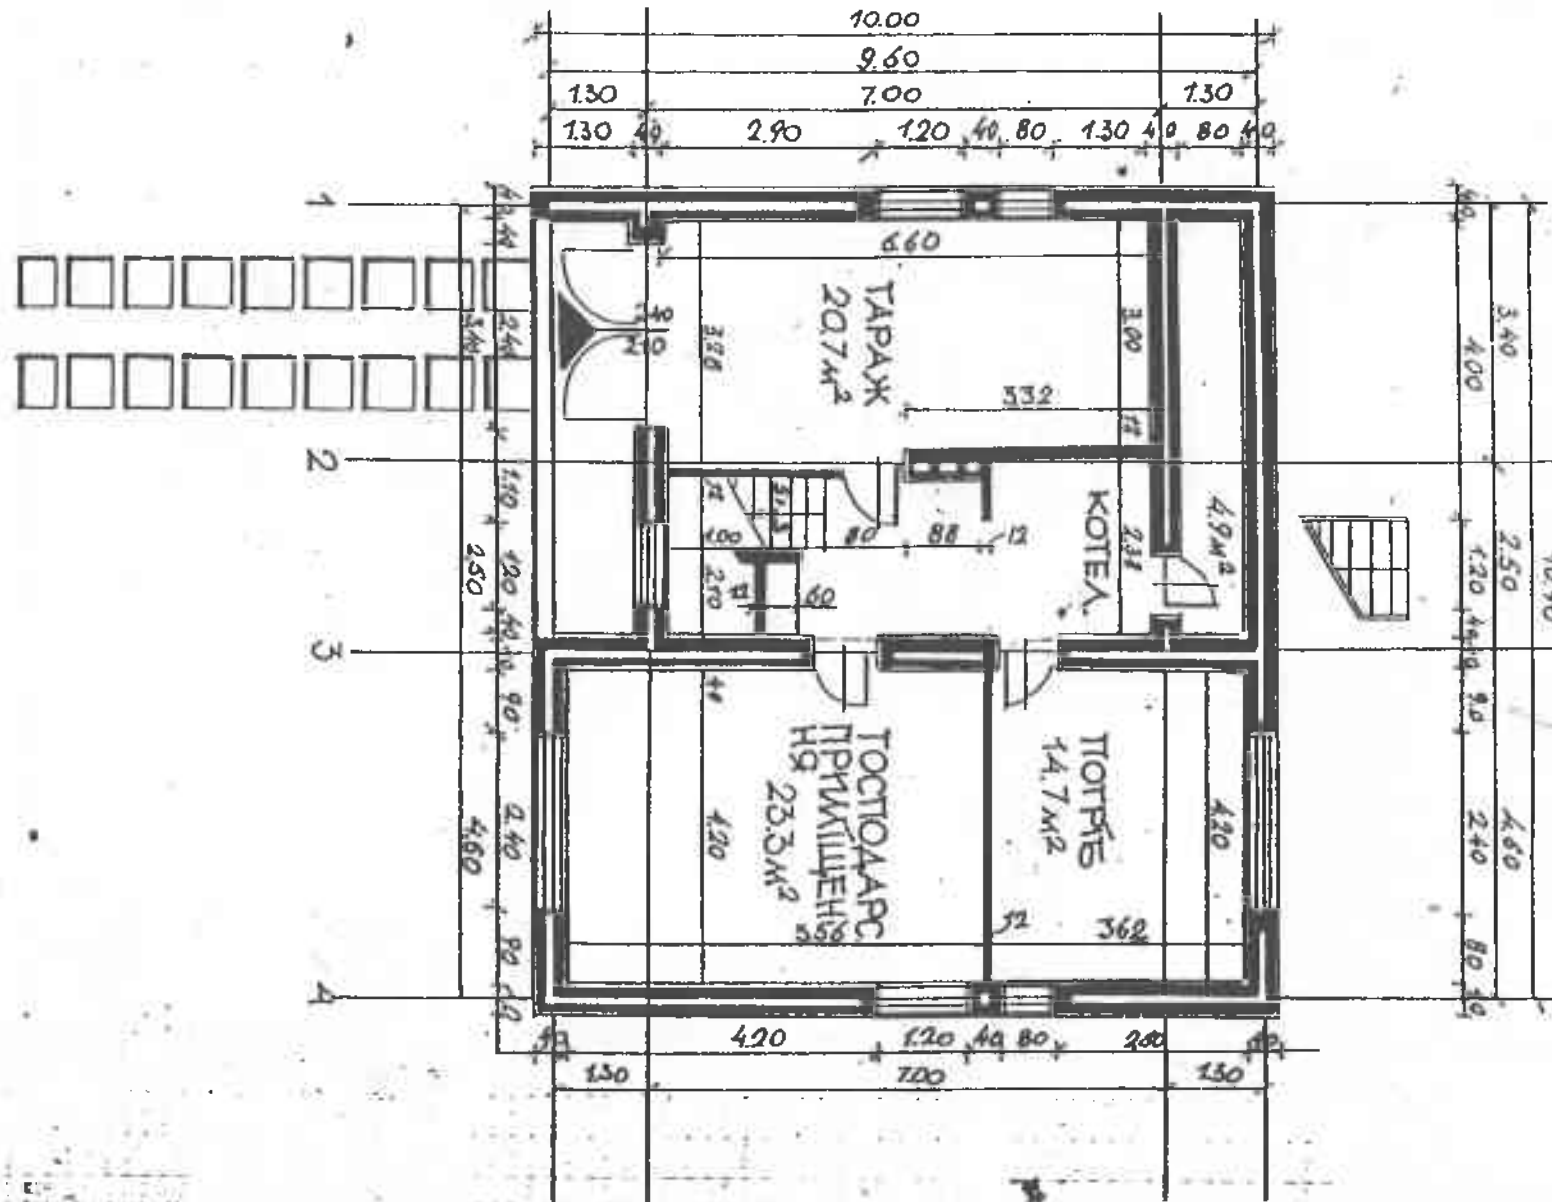

ПЛАН ПЕРШОГО ПОВЕРХУ ± 0.00

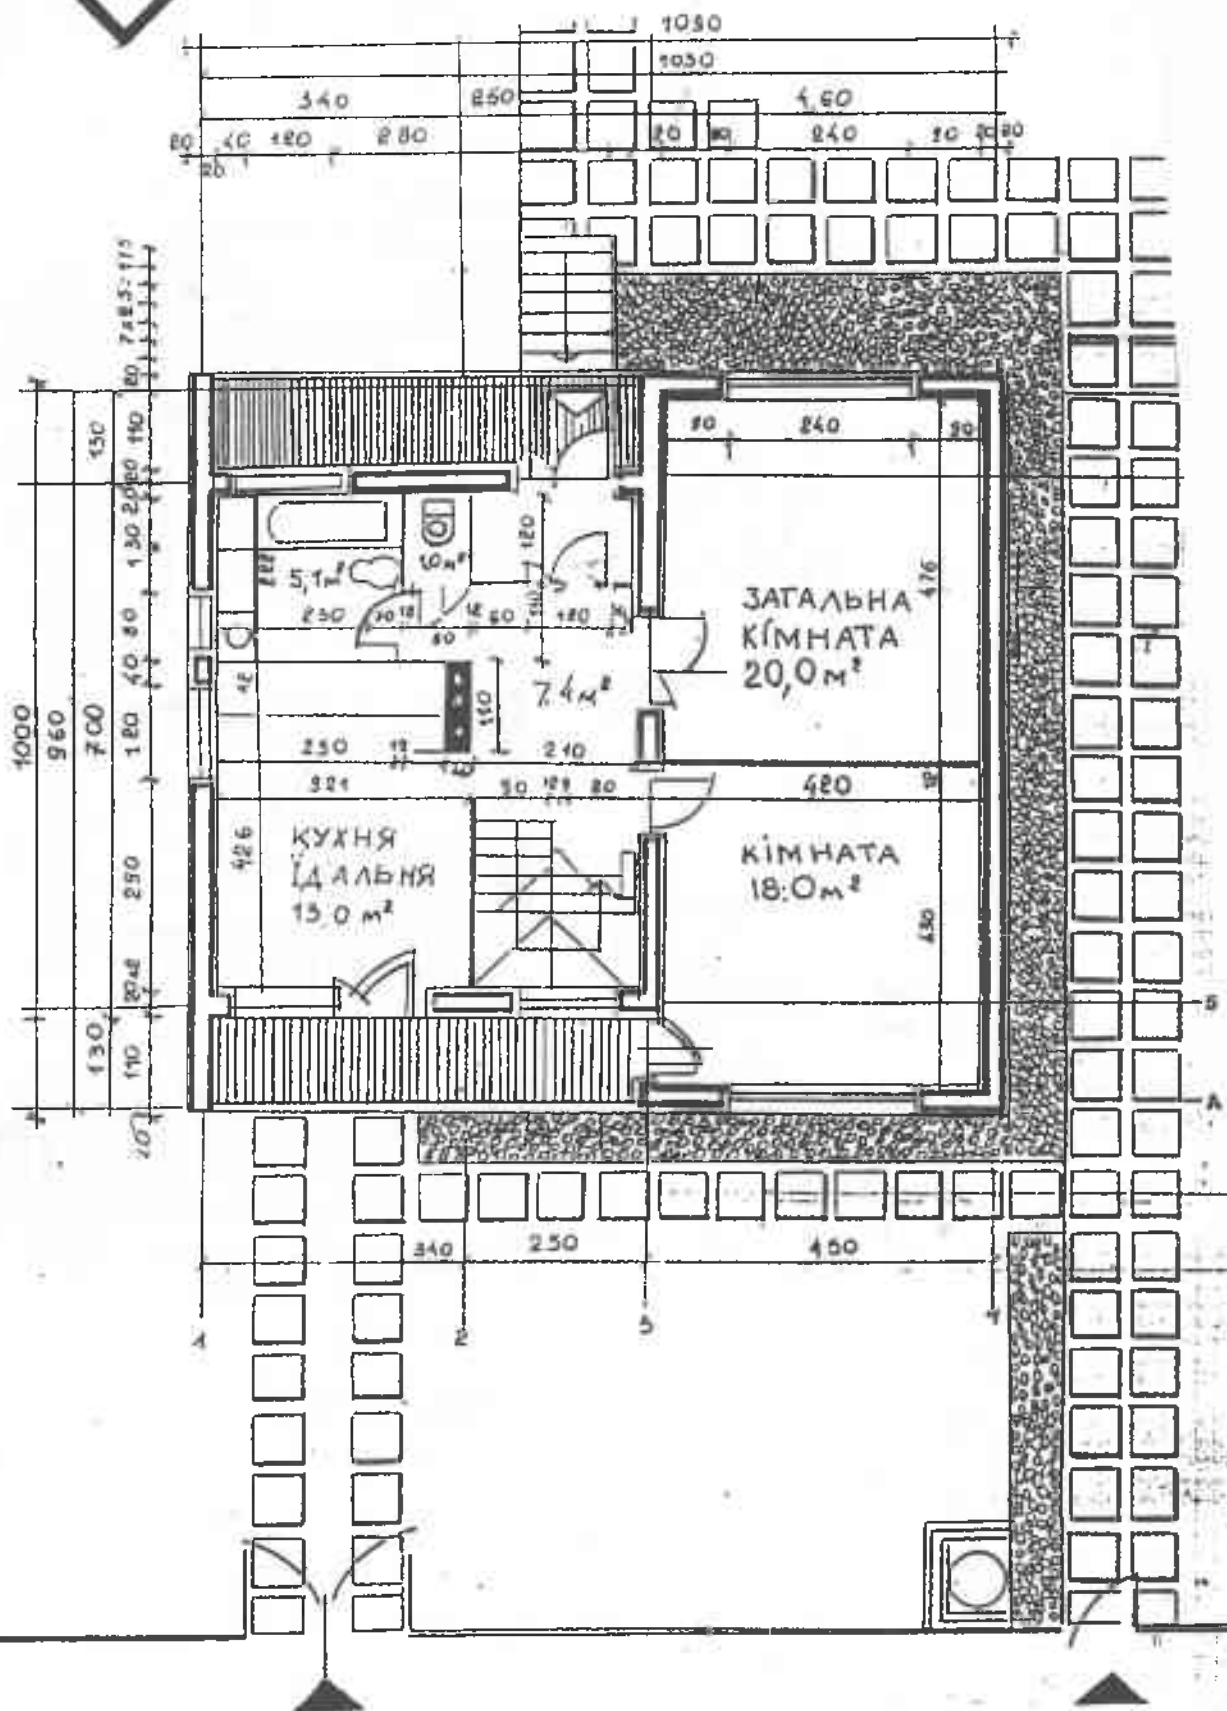

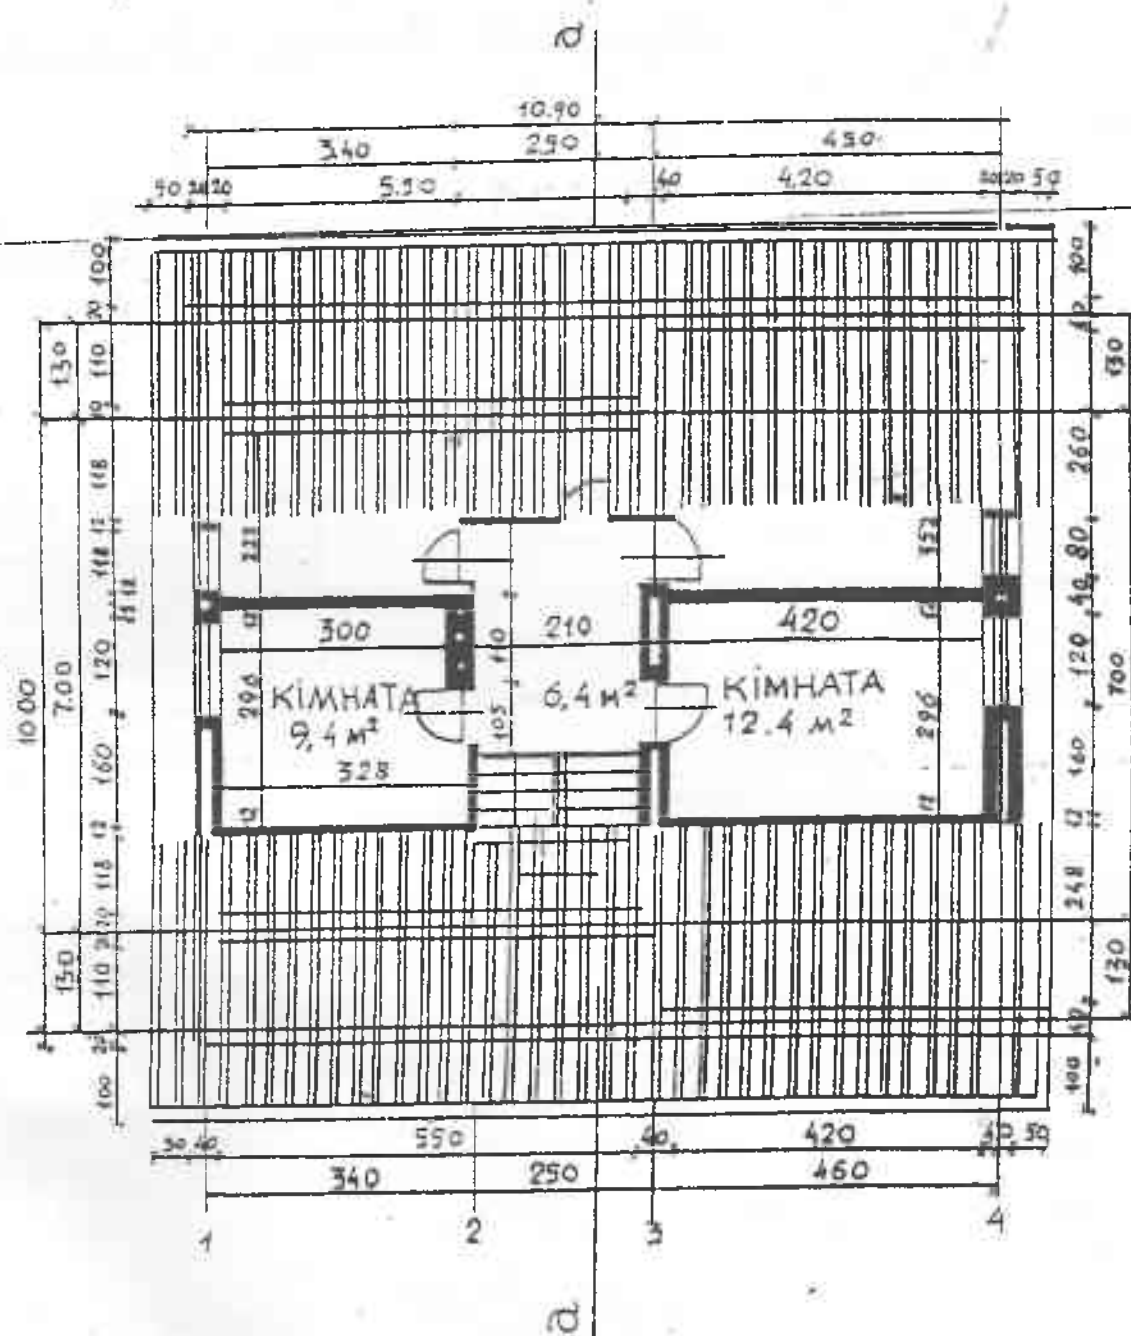

ПОЯСНЮВАЛЬНА ЗАПИСКА

до проекту реконструкції житлової ділянки

Яворському Дмитру Осиповичу

Житловий будинок по типовому проекту № ІНДІВ.

по індивідуальному проекту № 4 в районі Господарська будівля

кв. м. з господарськими приміщеннями: 1900

а) Господарська будівля

б)

загальною площею 1900 кв. м

Житловий будинок головним фасадом орієнтувати НА ПІВДЕННИЙ ЗАХІД

і розмістити на ділянці 1.2 м від чергової лінії. На ділянці зі сторони вулиці передбачається

огорожа висотою 1.2 м, вхід та проїзд на ділянку з вулиці ДО ЖИТЛОВОГО

БУДИНКУ пішохідна доріжка з ЖИТ. БУДИНКУ ДО Г/Б шириною 0.80 м.

Вздовж вулиці в межах виділеної ділянки влаштувати тротуар шириною 1.50

м. (дивись поперечний розріз вулиці)

РЕКОМЕНДАЦІЇ:

По житловому будинку:

Зовнішнє опорядження фасадів ОБЛИЦЬОВАТИ ОБЛИЦЬОВОЮ ЦЕГЛОЮ СТІН

Вікон та дверей ПОФАРБУВАТИ МАСЛЯНОЮ ФАРБОЮ У ВІДПОВІДНИЙ КОЛІР

Покрівлі ПОКРИТИ МЕТАЛОЧЕРЕПИЦЕЮ

Господарські приміщення ОБЛИЦЬОВАТИ ОБЛИЦЬОВОЮ ЦЕГЛОЮ СТІН

ПОКРІВЛІ ПОКРИТИ МЕТАЛОЧЕРЕПИЦЕЮ.

Інженерне обладнання:
водопровід ШАХТНИЙ КОЛОДЯЗЬ
каналізація БЕТОННО ВИГРІБНА ЯМА
газифікація ЗГІДНО ТУ
радіофікація ЗГІДНО ТУ
телебачення ЗГІДНО ТУ
опалення ПІЧНЕ

ІНШІ ВИМОГИ:

ПОТРИМУВАТЦЯ ВИМОГ
БУДІВЕЛЬНОГО ПАСПОРТУ

ПРИМІТКА; 1. В разі відсутності централізованої каналізації передбачити автономну каналізацію шляхом тупування септика та фільтруючого колодезя.

Проект забудови земельної ділянки розробив
інженер АПГ Р. Лещук

АКТ

виносу в натуру земельної ділянки і розбивки будівель

від КВІТЕНЬ 200 7 р.

Я, ЛОФІЇ Р.М. представник головного архітектора міста, районного архітектора на підставі рішення Яворської

міської, селищної, сільської Ради від 16.01. 200 7 р. № 99 і у відповідності з проектом

забудови земельної ділянки в присутності представника міської, селищної, сільської Ради ІГНАЦЕВИЧА С.С.

встановив в натурі межі земельної ділянки, виділеної громадянину Яворському Дмитру Осиповичу прізвище, ім'я та по батькові

для будівництва індивідуального дачного житлового будинку і господарських будівель.

Площа земельної ділянки становить 1900 кв.м. Земельна ділянка знаходиться в місті, смт., селі

ЯВОРА

по МА „ВАРУШ“ буд. №

земельна ділянка межує з ділянкою громадянина ІВАНІЦЬКОЇ О. прізвище, ім'я та по батькові власників ділянок

або кому належить вільна від забудови ділянка, орієнтація по сторонах світу.

В. Одночасно з виносом меж земельної ділянки проведено винос вісей дачного житлового будинку за проектом № ІНА.ІВ. і господарських будівель за проектом № ІНА.ІВ. відмітка підлоги дачного житлового будинку становить

репера за репер прийнято

Межі земельної ділянки і розбивки вісей будівель закріплені на місцевості знаками і передані забудовнику на збереження. (Схема виносу в натуру меж земельної ділянки і розбивки вісей будівель на звороті.

Без схеми акт не дійсний.

Межі ділянки і будівлі встановив: ЛОФІЙ Р. підпис

Межі ділянки і будівлі прийняв: ЯВОРСЬКИЙ Д. підпис

Представник Ради ІГНАЦЕВИЧ С. підпис

ДОЗВІЛ № 26

на право закладки фундаментів під індивідуальне будівництво

Від "224" травня 2007 року № 261

Головний архітектор міста

Інспектор Держархбудконтролю Турківського району

дозволяє громадянину Яворському Дмитру Осиповичу приступити

до закладки фундаментів індивідуального ОДНО поверхового

(мансардного (дачного) житлового будинку за проектом № ІНАДІВ. та господарської

будівлі за проектом № ІНДІВ. згідно з планом земельної ділянки по вул.

буд. № _____ в місті, селі ЯВОРА

на підставі рішення сесії Явірської сільської ради

Від 16 01 200 7 р. № 99

акту виносу в натуру меж земельної ділянки і розбивки будівель від КВІТЕНЬ 200 7 року.

Дата початку будівництва фундаментів ТРАВЕНЬ 200 7 р.

Забудовник зобов'язаний після завершення будівництва фундаментів звернутися до головного архітектора міста, районного архітектора за здійсненням прийняття виконаних робіт та отримання дозволу на завершення індивідуального будівництва.

Забудовник відповідає:

1. За правильність розміщення (дачного) житлового будинку і господарських будівель згідно з затвердженим планом земельної ділянки.

2.3а порушення розмірів фундаментів.



Головний архітектор міст
Інспектор ДАБК

Беседин 1.1.

Я, забудовник Яворський А. О. з порядком здійснення індивідуального будівництва у Львівській області ознайомився.

Забудовник Яворський А.О.

підпис